

# GAMBAR RENCANA TAPAK RINCI (SITE PLAN)

## A. ARAHAN PEMANFAATAN LAHAN

- Luas lahan Awal
- Luas Lahan Penambahan
- Luas Lahan Keseluruhan
- Daerah Sempadan Pagar
- Luas lahan yang dapat dimanfaatkan
- Luas lahan efektif
- Luas lahan prasarana dan sarana
- ketinggian bangunan maksimal

-DSP

15,715 M2  
5,050 M2  
20,765 M2  
387 M2  
20,378 M2 / 100%  
12,227 M2 / 60%  
8,151 M2 / 40%  
2 Lt. / 12 M'

## B. PERINCIAN PEMANFAATAN LAHAN SITEPLAN LAMA

No. 651.2/203-RT.DTR/2013  
Tanggal 30 April 2013

## B. PERINCIAN PEMANFAATAN LAHAN

- Luas Lahan Efektif

| NO.      | URAIAN (Blok)   | LUAS (M2) | KET.       |
|----------|-----------------|-----------|------------|
| 1        | INDUSTRI 1      | 5,520     | Revisi     |
| 2        | KANTOR          | 350       | Penambahan |
| 3        | GUDANG LUAR     | 1,152     | Penambahan |
| 4        | R. OVEN         | 288       | Penambahan |
| 5        | R. DEMPUL       | 216       | Revisi     |
| 6        | MESS & MUSHOLLA | 100       | Revisi     |
| 7        | SELASAR         | 581       | Penambahan |
| Jumlah I |                 | 8,207     | 40.27%     |


- Luas Lahan Prasarana dan Sarana

| NO.       | URAIAN                  | LUAS (M2) | KET.   |
|-----------|-------------------------|-----------|--------|
| 1         | Taman / RTH             | 5,345     | Revisi |
| 2         | Tandon Air              | 225       | Revisi |
| 3         | Jalan, Saluran & Parkir | 6,601     | Revisi |
| JUMLAH II |                         | 12,171    | 59.73% |


- JUMLAH TOTAL I + II 20,378 M2 / 100%

## Keterangan :

- Luas Areal Yang Dimohon
- Luas Areal Revisi / Penambahan
- Taman / RTH
- Tandon Air
- GSP: Garis Sempadan Pagar
- GSB: Garis Sempadan Bangunan
- GSBS: Garis Sempadan Bangunan Samping
- GSBB: Garis Sempadan Bangunan Belakang

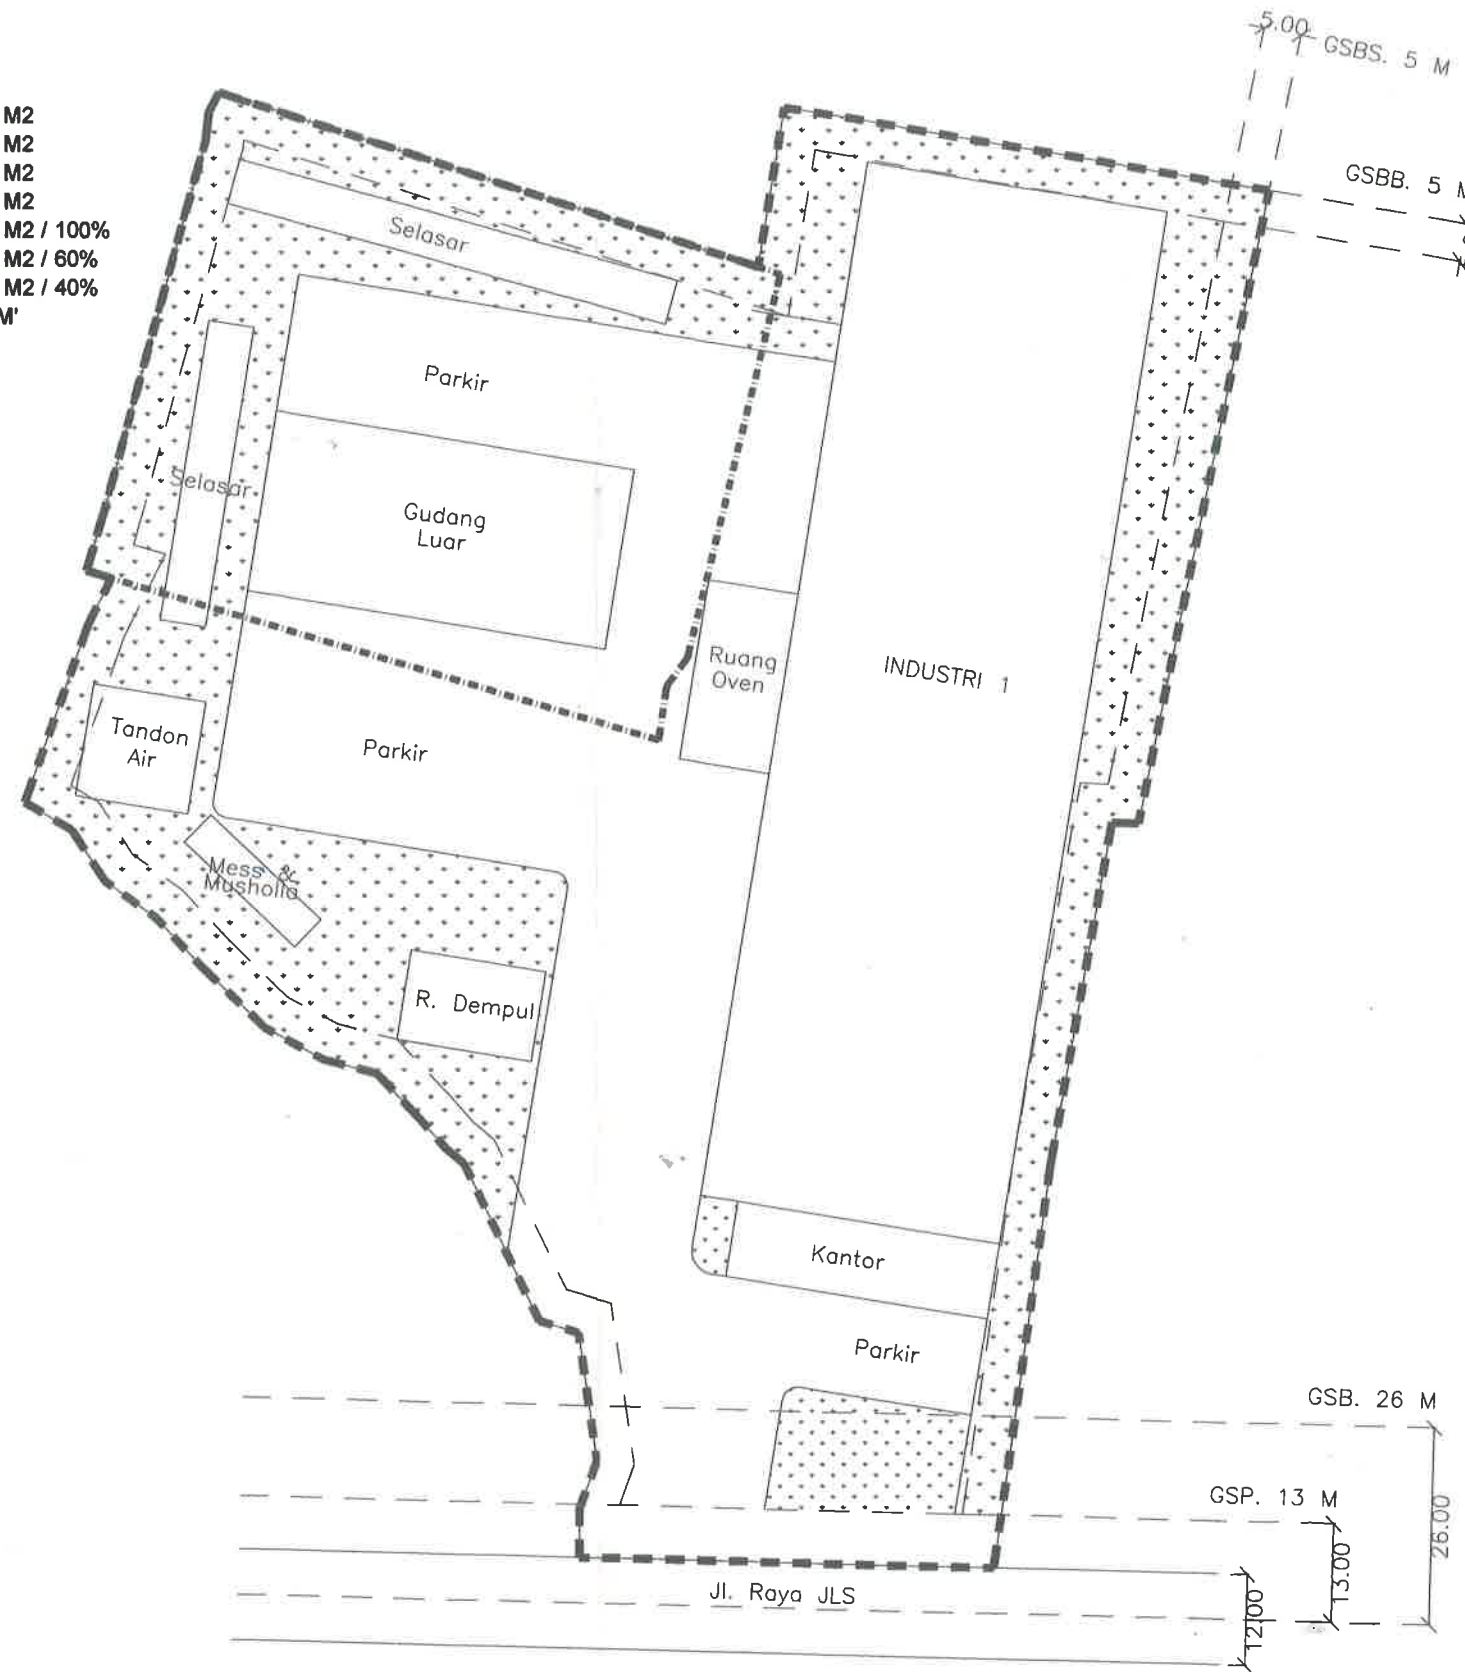

Lampiran  
Pengesahan Rencana Tapak Rinci (Site Plan)  
Nomor : 651.2/1589-RT.DTR  
Tanggal : 09 November 2016

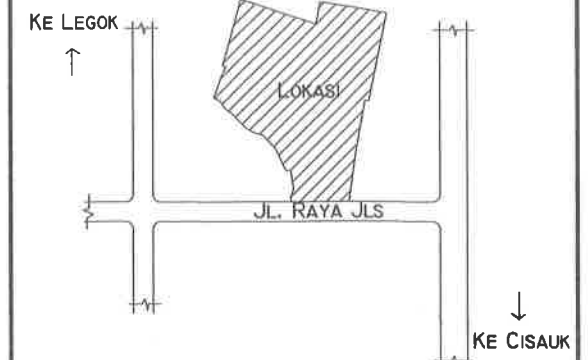

KEY PLAN LOKASI YANG DIMOHON

PEMOHON  
PT. MEGA TRUKINDO UTAMA

HERIYANTO  
DIREKTUR  
PT. MEGA TRUKINDO UTAMA  
TANGERANG

Disahkan,  
KEPALA DINAS TATA RUANG  
KABUPATEN TANGERANG

Ir. H. ILHAM CHAIR, MM.  
NIP. 195801031993031001

DIPERIKSA DAN DISETUJUI :

DISETUJUI

DIPERIKSA

SEMATA - MATA HANYA MENYATAKAN RENCANA PERUNTUKAN  
TIDAK MENYATAKAN HAK ATAS TANAH

RENCANA TAPAK RINCI (SITE PLAN)

INDUSTRI KAROSERI  
(REVISI & PENAMBAHAN)  
DESAKEL CARINGIN, KEC. LEGOK

SKALA 1 : 1.000

PEMERINTAH KABUPATEN TANGERANG  
DINAS TATA RUANG  
KOMPLEK PERKANTORAN TIGARAKSA  
TEP. (021) 5991510, 5991514 FAX (021) 5991514  
TIGARAKSA - TANGERANG